



Selected **Works**
Déborah **Tsogbé**

/Zuciya/

home as hearth








Partnered work in designing modular, adaptable construction methods for displaced communities in north east Nigeria.

I am responsible for concept design, 3d model, construction diagram, sections, elevations and perspectives. Done with AutoCAD, Rhino and Adobe Illustrator.

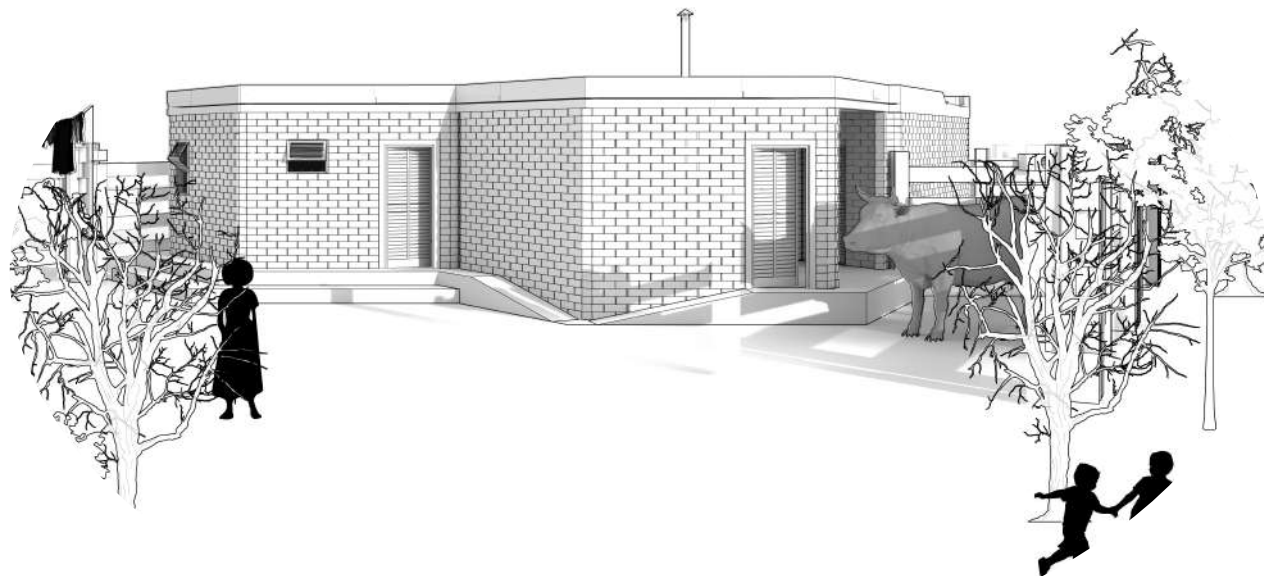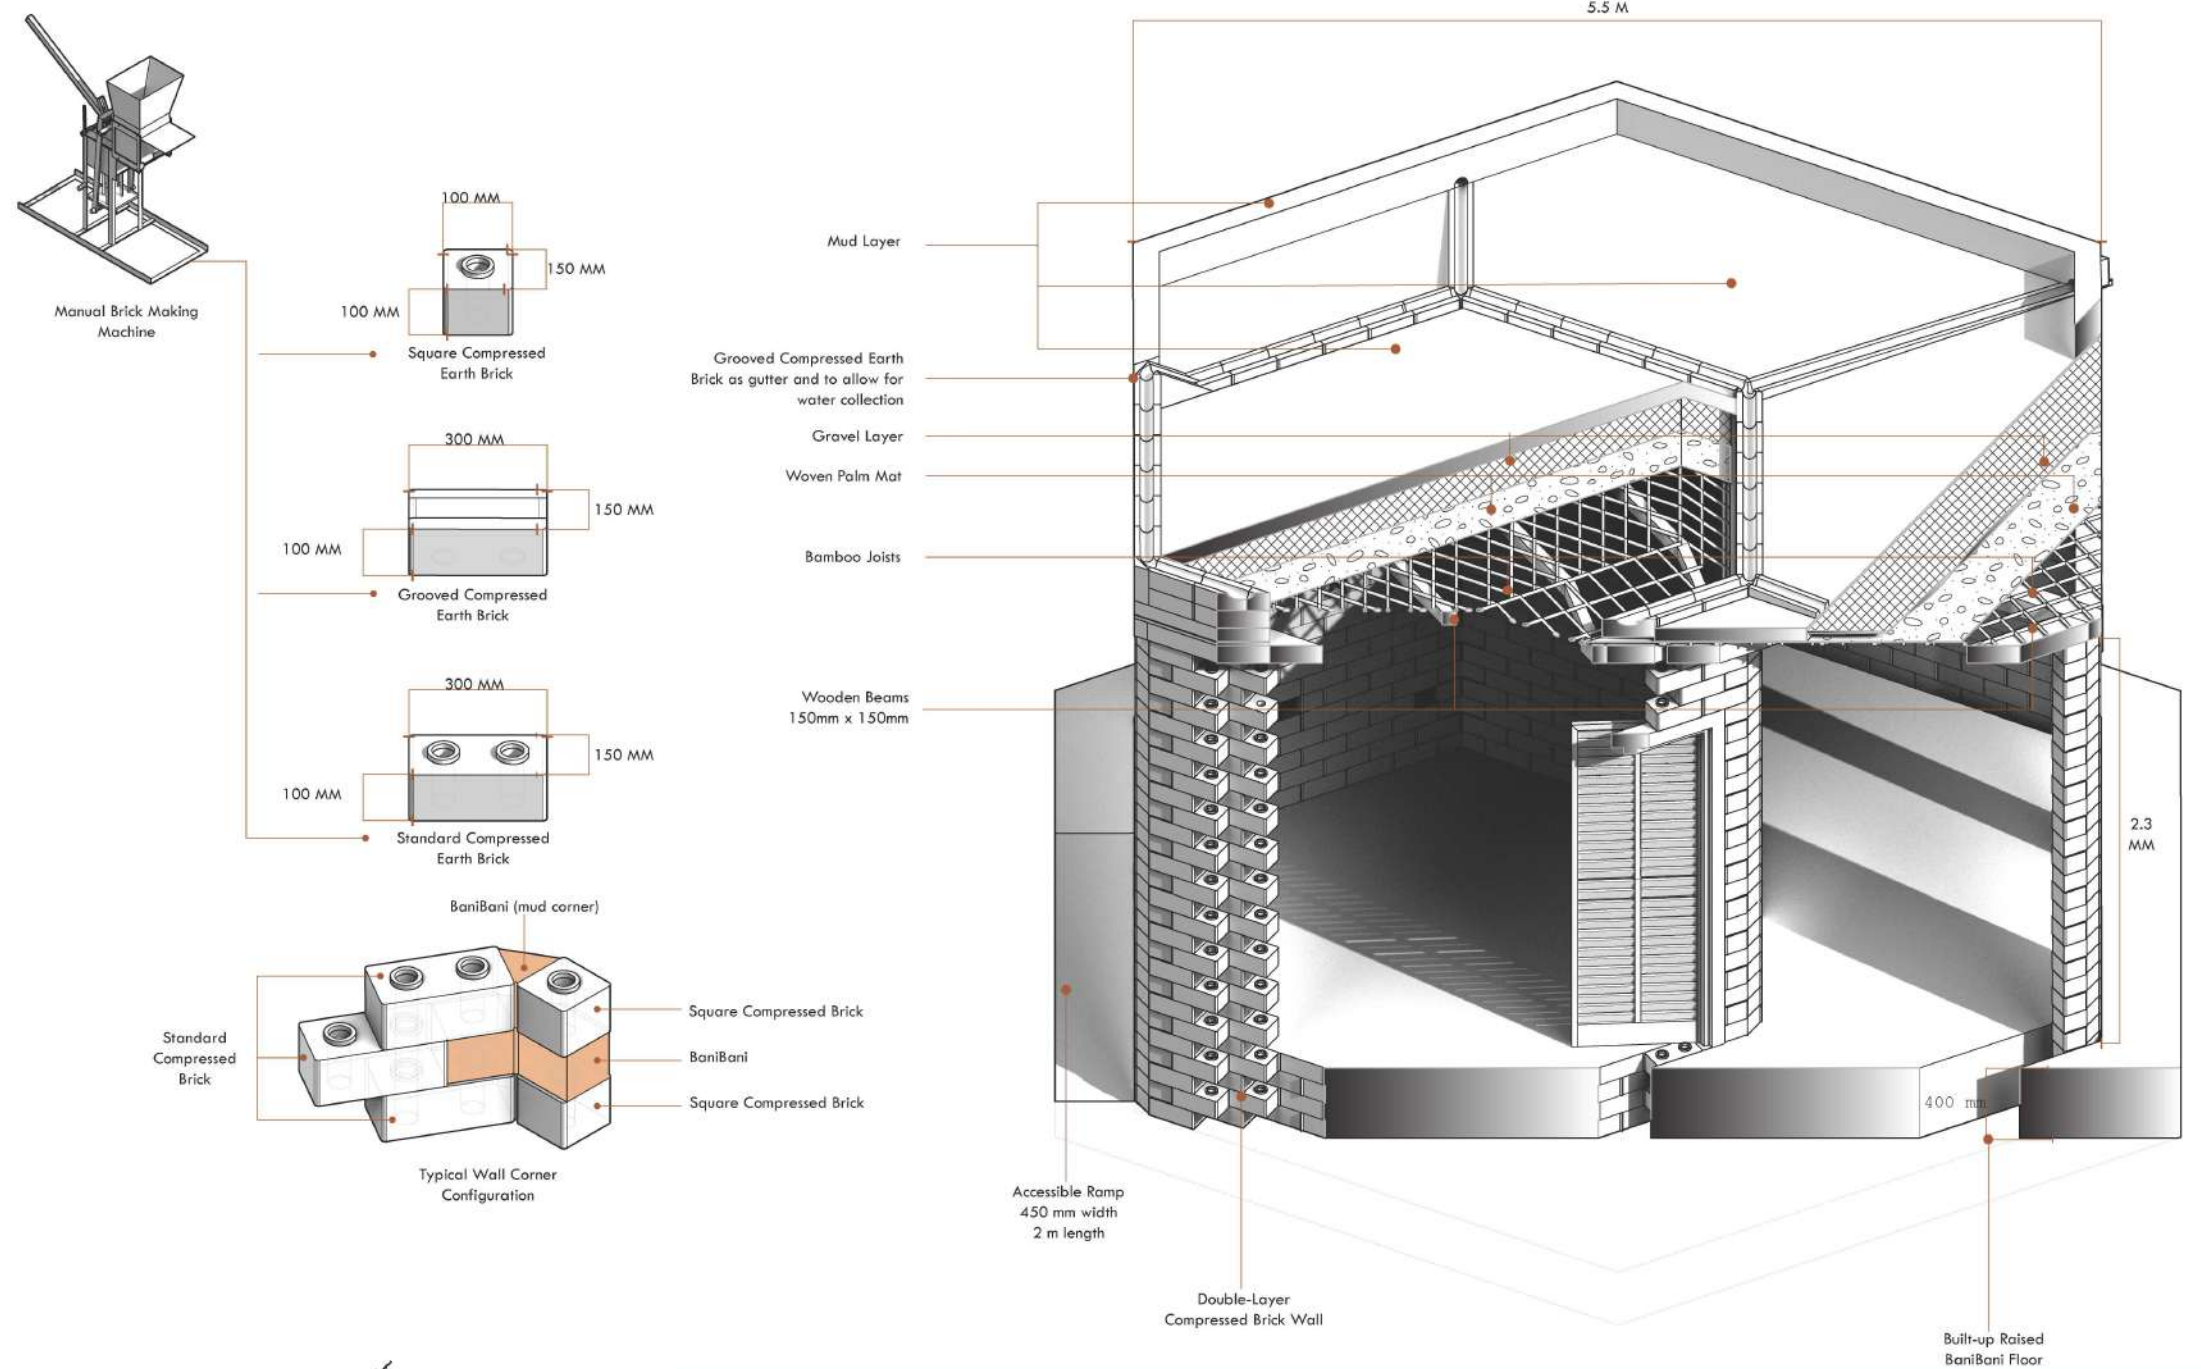


Typical /Zuciya/ Module - Construction






The Zuciya module is comprised of materials that can be found easily in North Eastern Nigeria - Bani Bani (mud) used for the angled corners, compressed interlocking earth blocks using a QMR2-40 Manual Block making machine. The blocks can then be reinforced using a mortar mixture. For the roof, traditional construction has been adapted, resulting in layers of wooden beams for structure, Bamboo joists, woven palm mat, gravel and a final layer of bani bani (mud). This is a low cost, accessible method of construction suitable for the savanna ecosystem of the area.

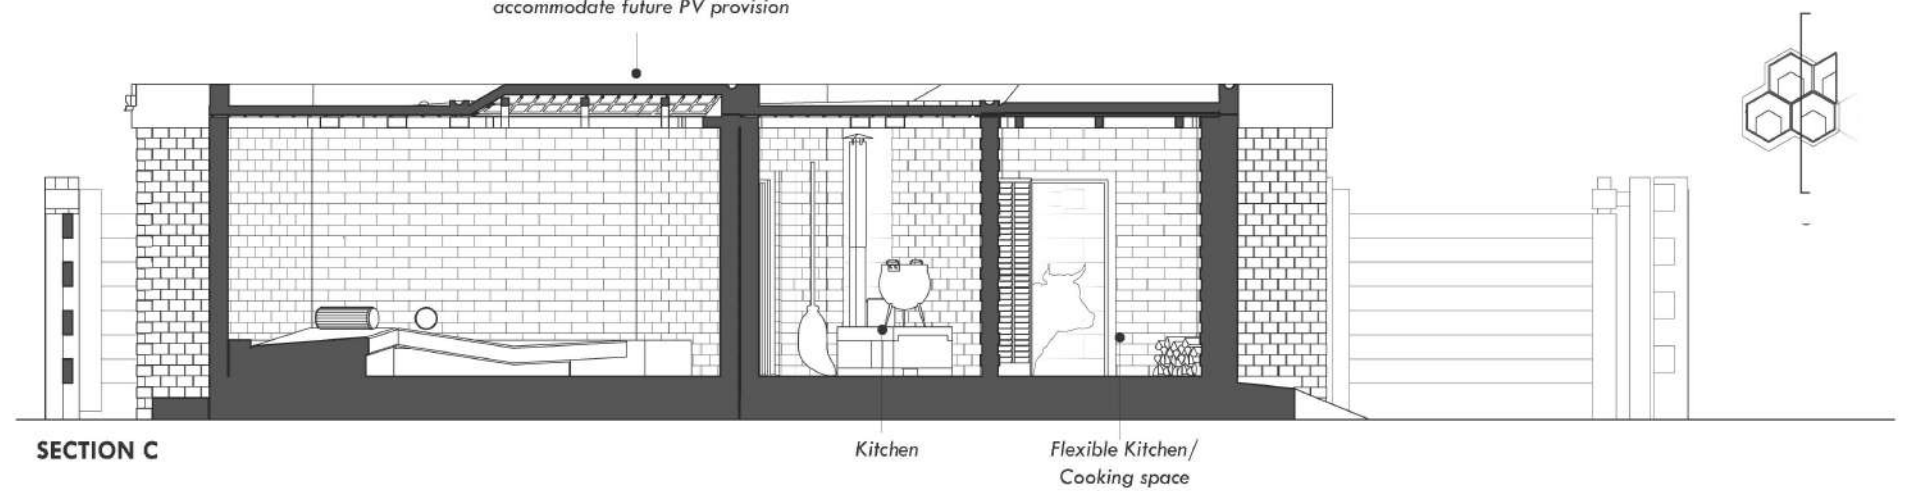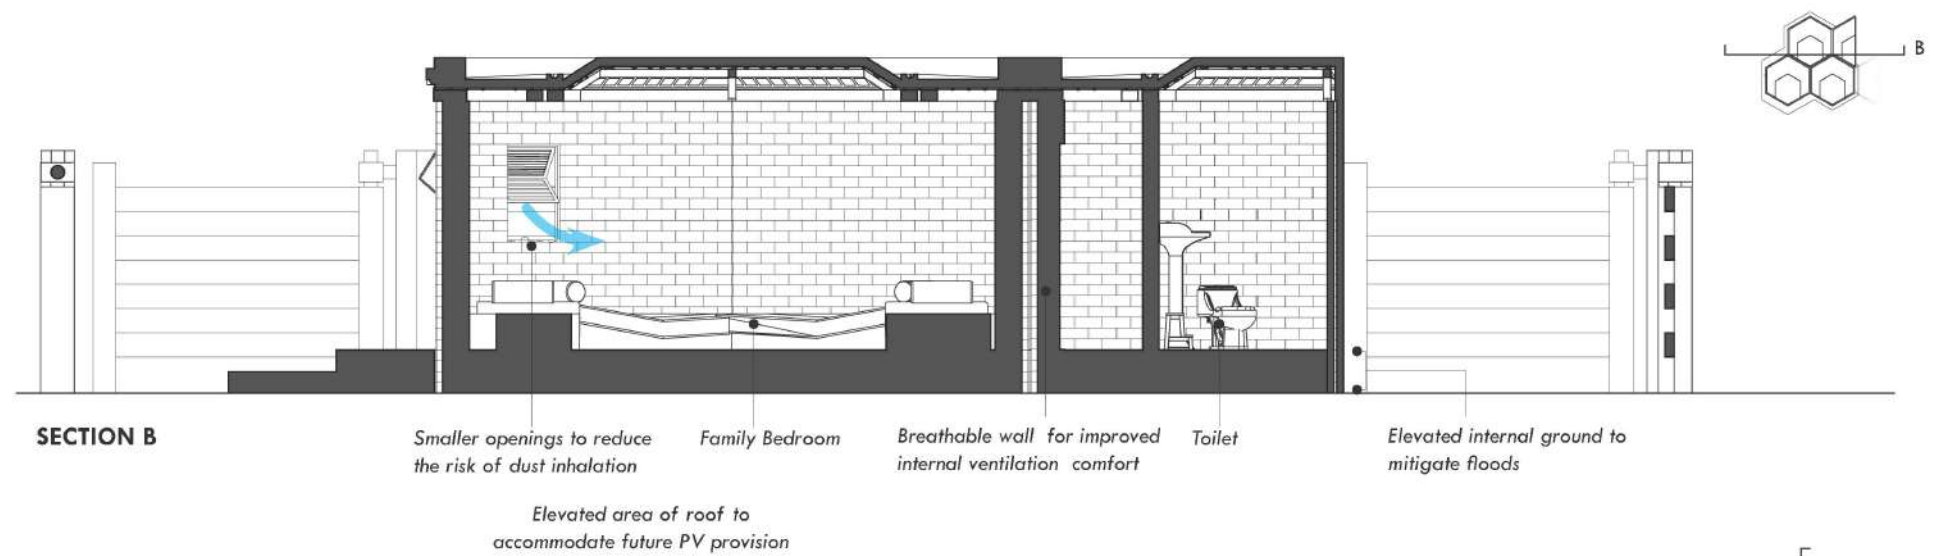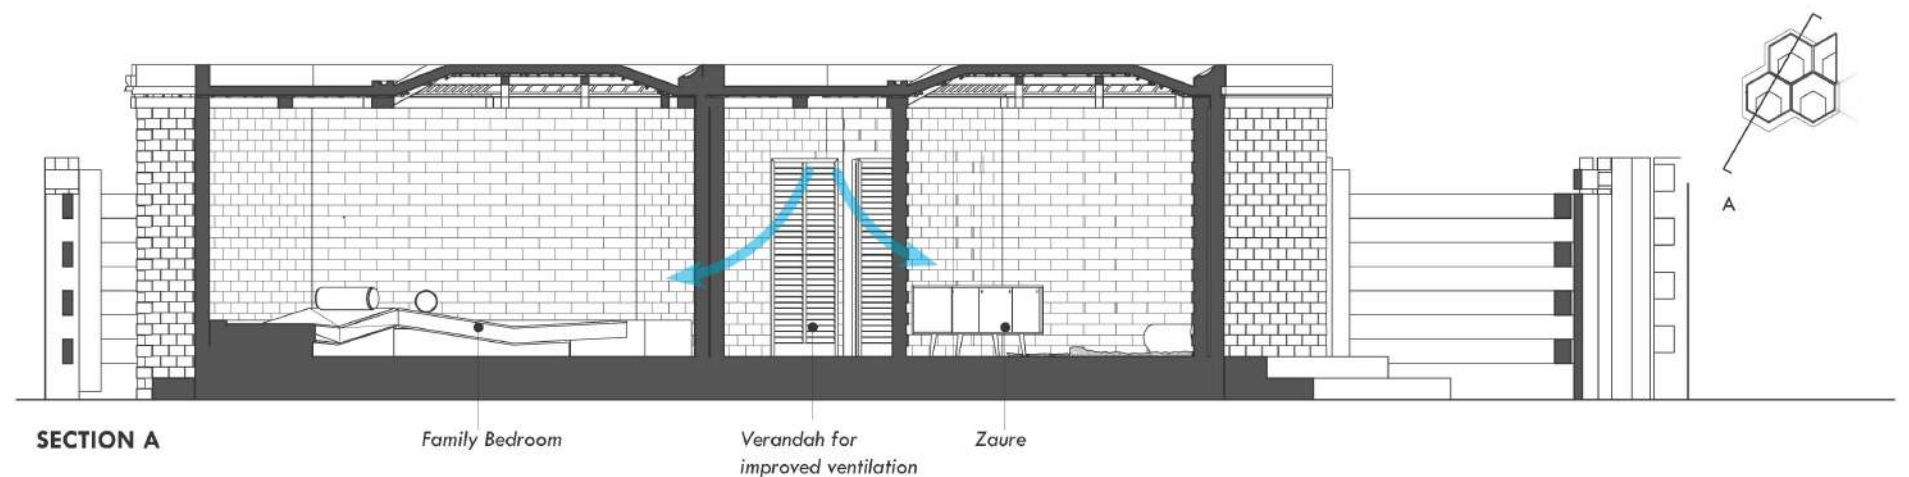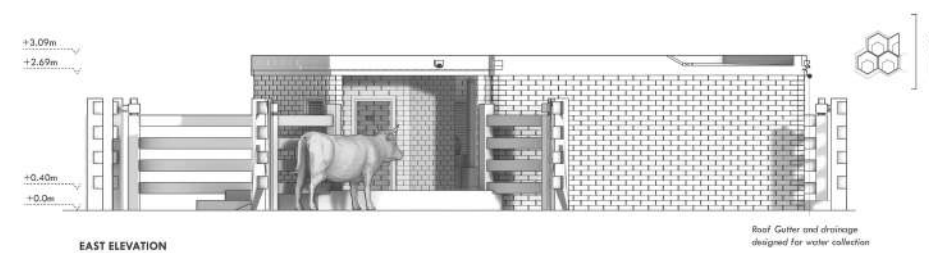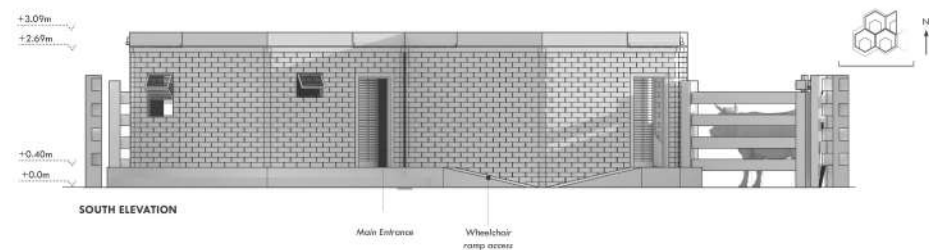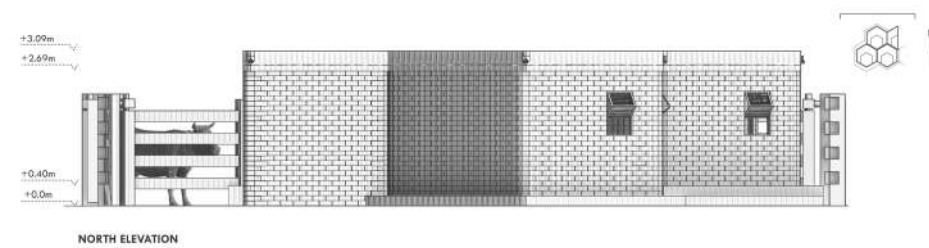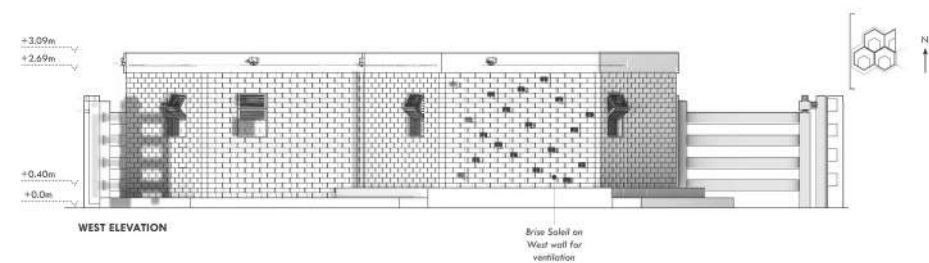



interior elevations

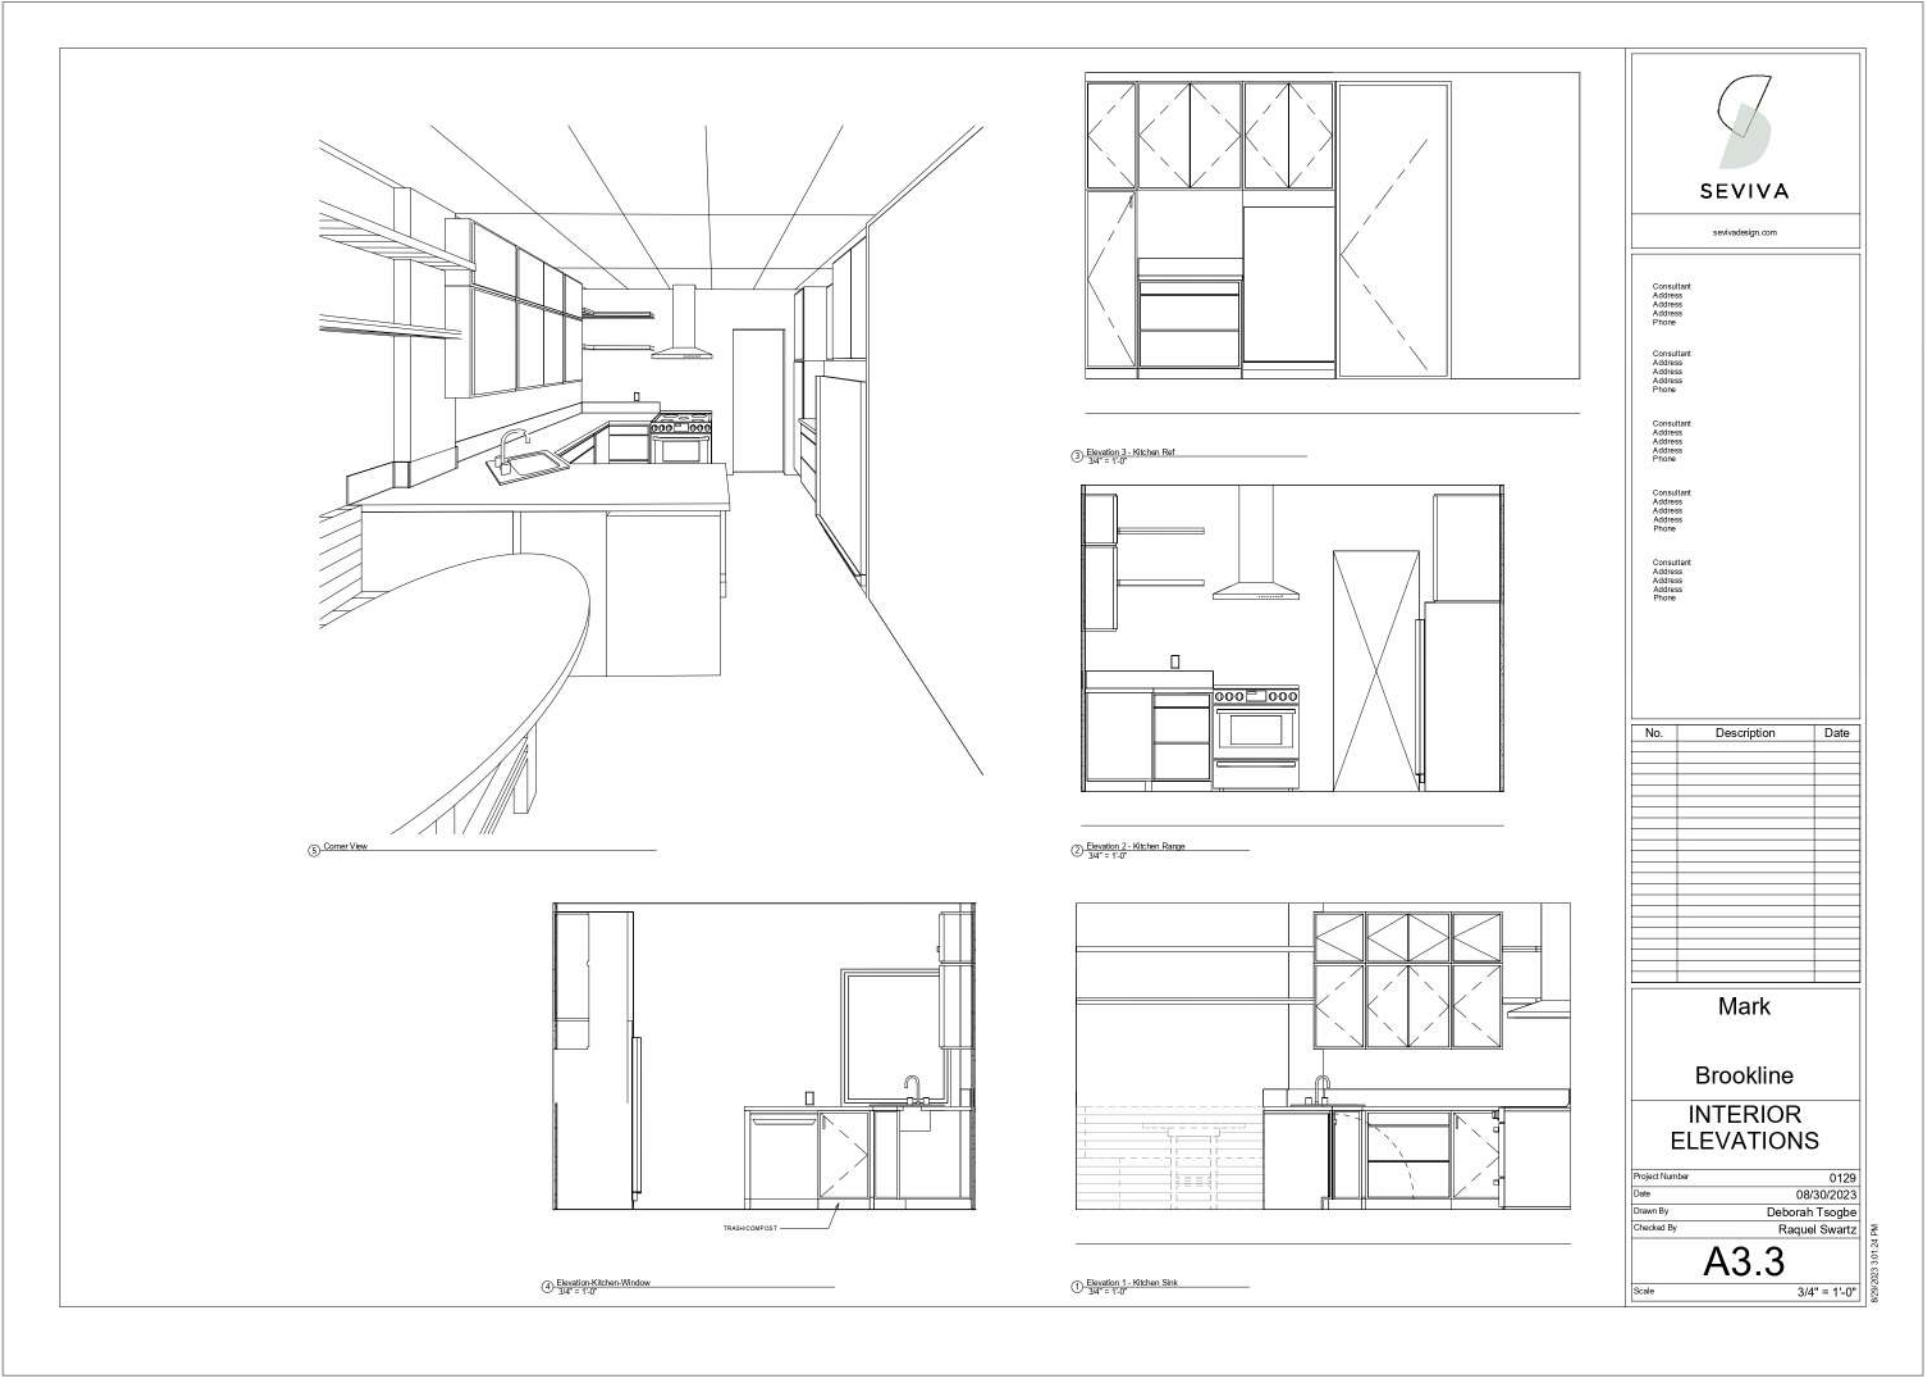

Part of contract work with Kadjoli Home Park. Kitchen renovation with deliverables including renders and elevations. For private client in Lomé, Togo. Done with Rhino and GIMP.

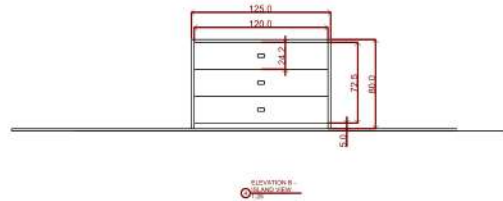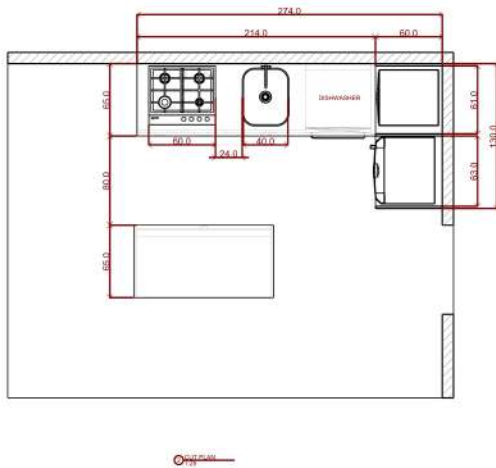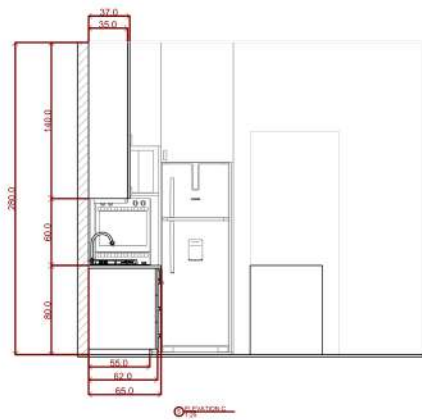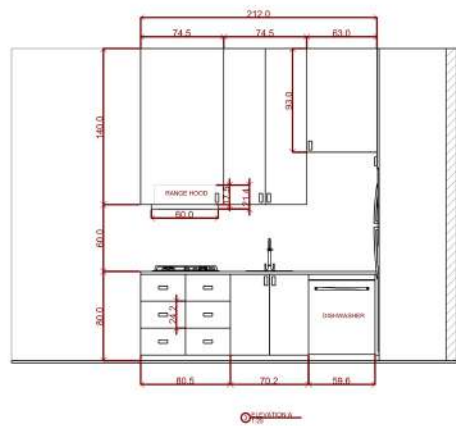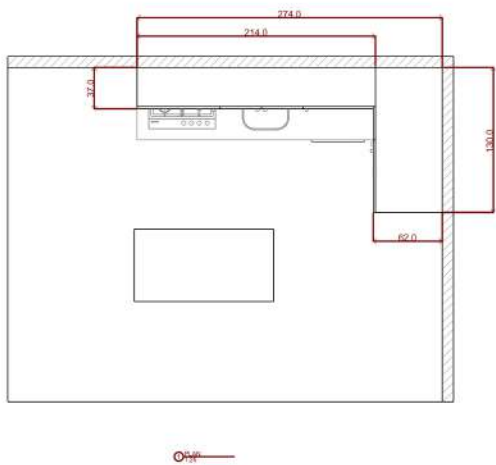


Grief House

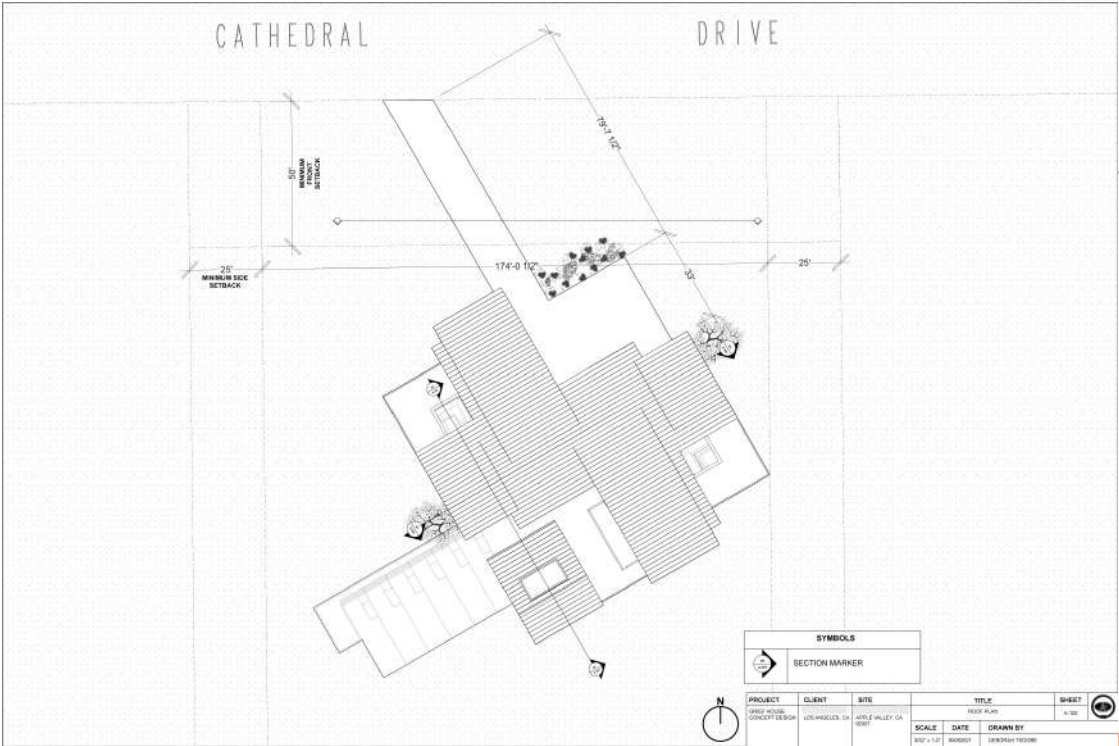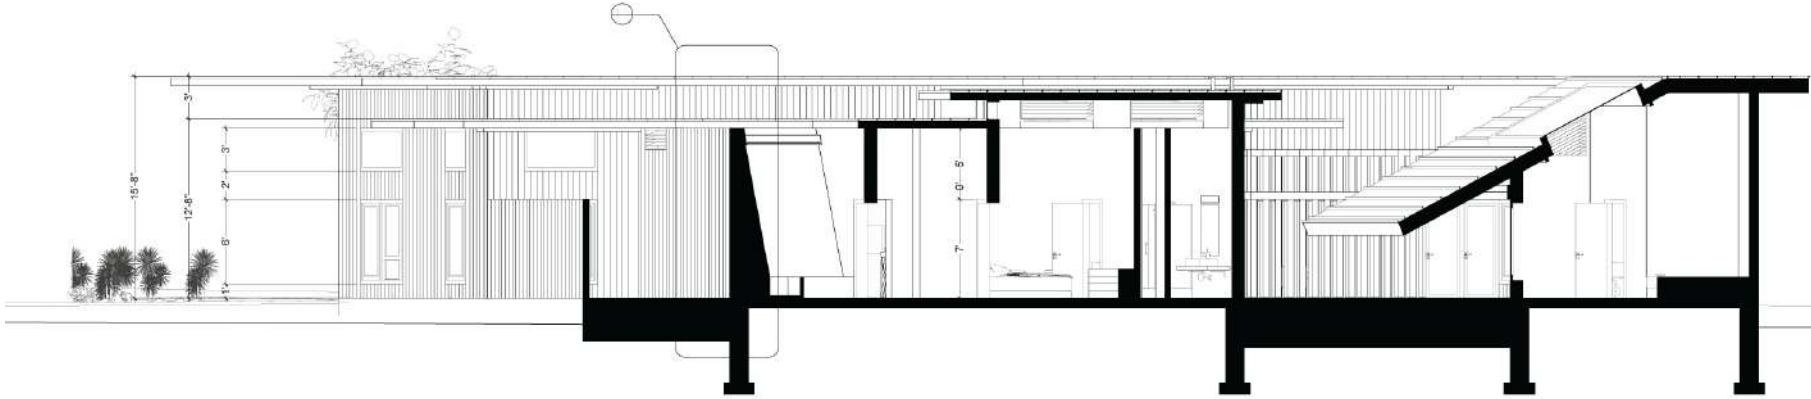

PROJECT	CLIENT	SITE	TITLE		SHEET	
GRIEF HOUSE CONCEPT DESIGN	LOS ANGELES, CA	APPLE VALLEY, CA 92307	SECTIONS		A-301	
			SCALE	DATE	DRAWN BY	
			1/4" = 1'-0"	3/05/2021	DEBORAH TSOGBE	


Client work; concept design and drawing set detailing a single family home in Southern California. Delivered renderings, architectural drawings and diagrams. Done with AutoCAD, Rhino 3d, Adobe Illustrator, and Vray.

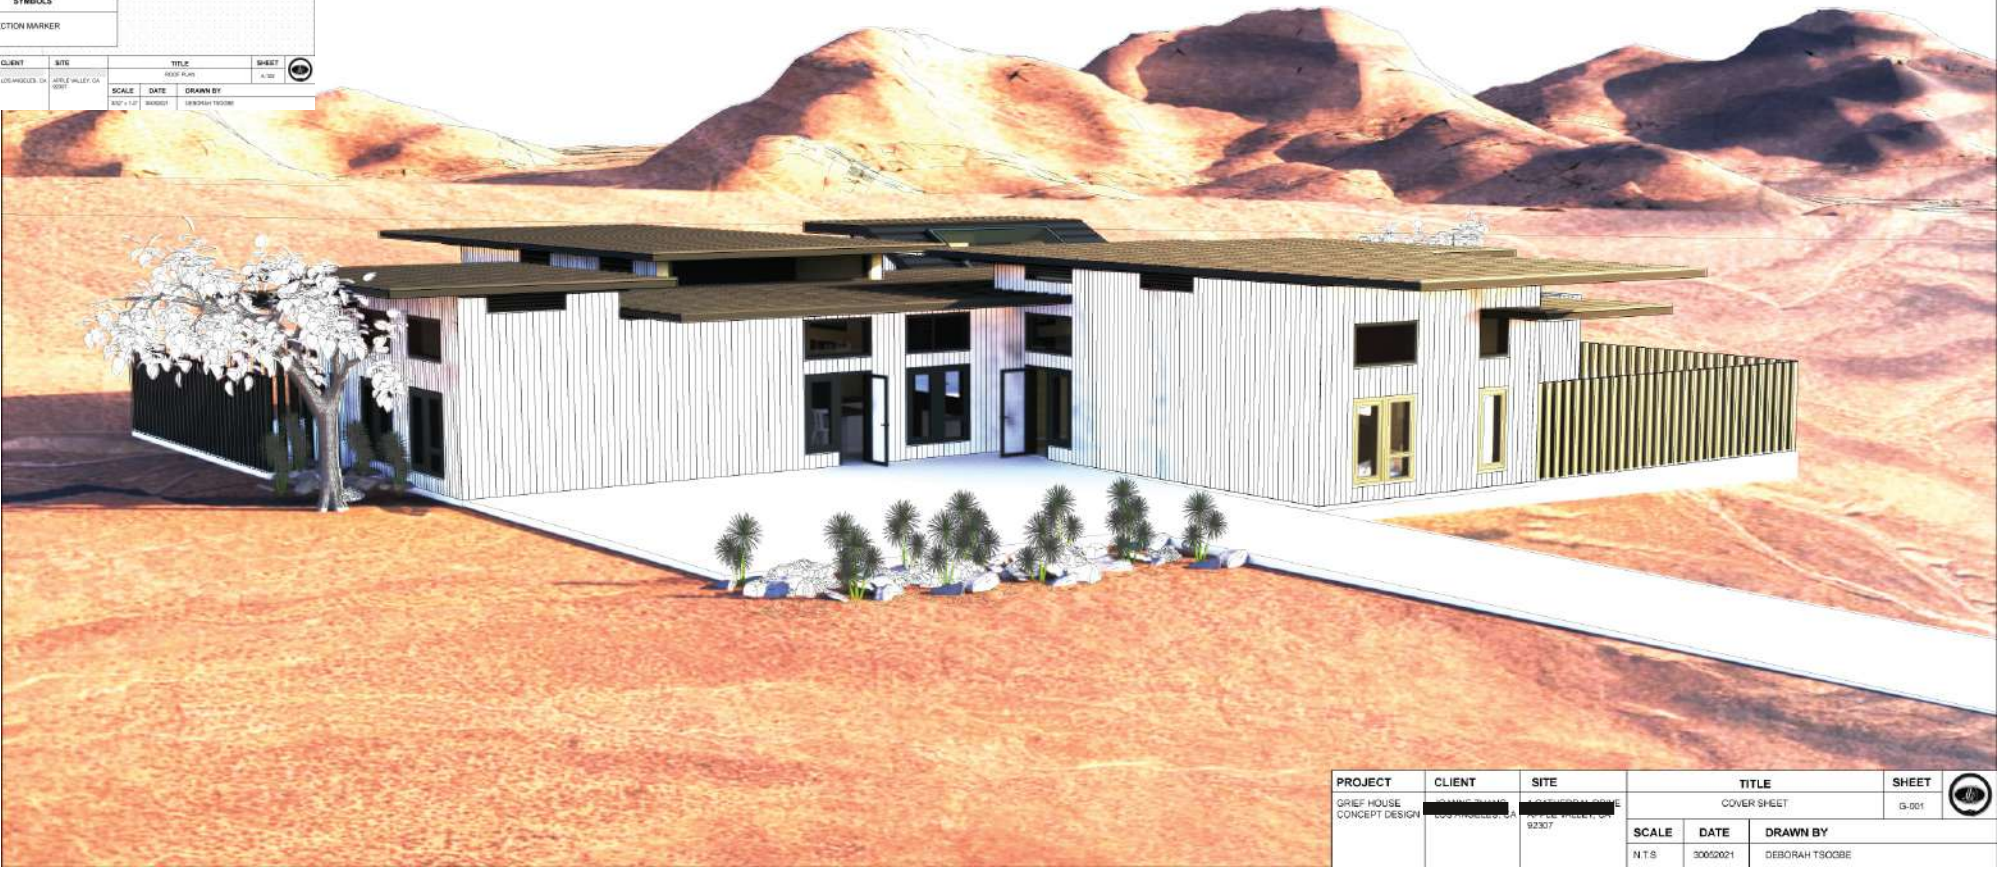




WEST ELEVATION

1/4" = 1'-0"

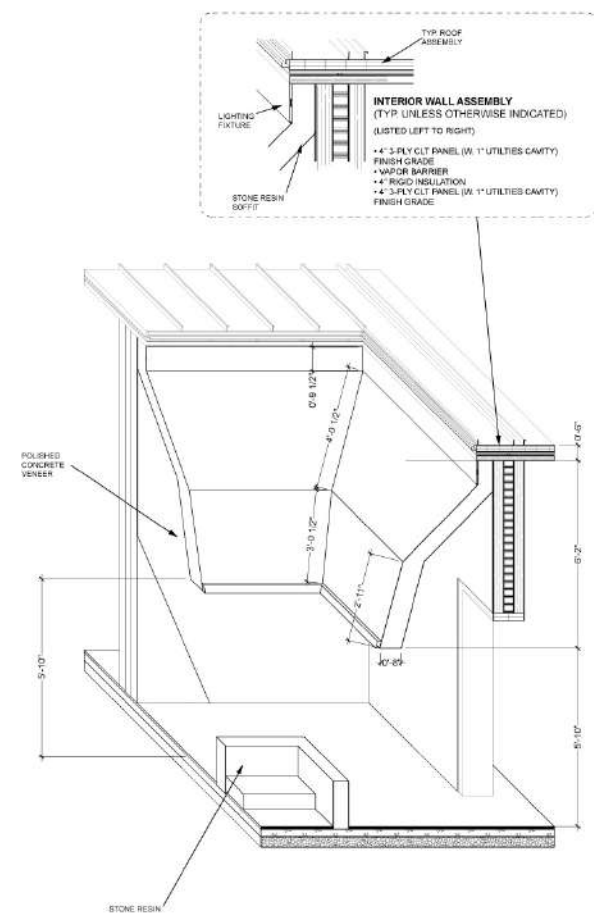

D3 - EAST SPA DETAIL



1/2" = 1'-0"

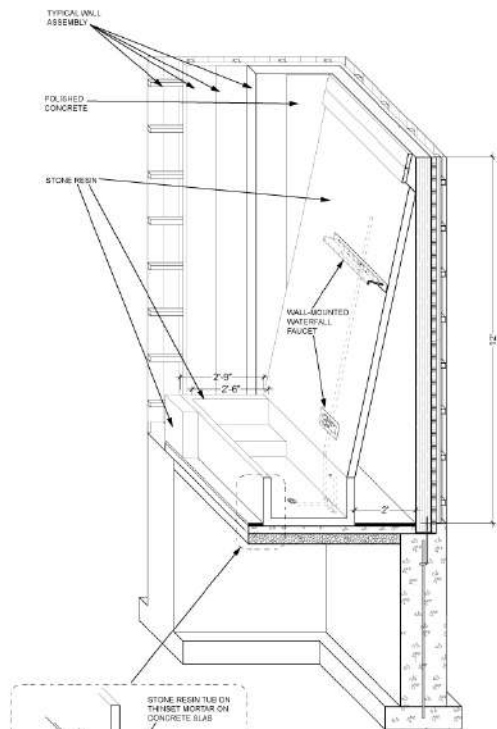

D2 - WEST SPA DETAIL

1/2" = 1'-0"

ROOF ASSEMBLY
(TYP. UNLESS OTHERWISE INDICATED)

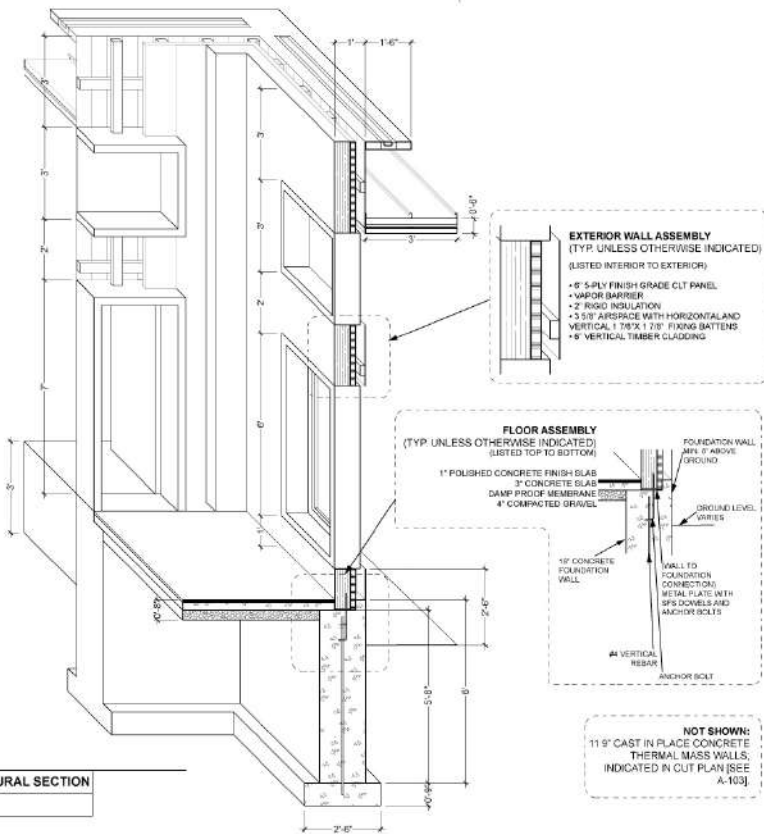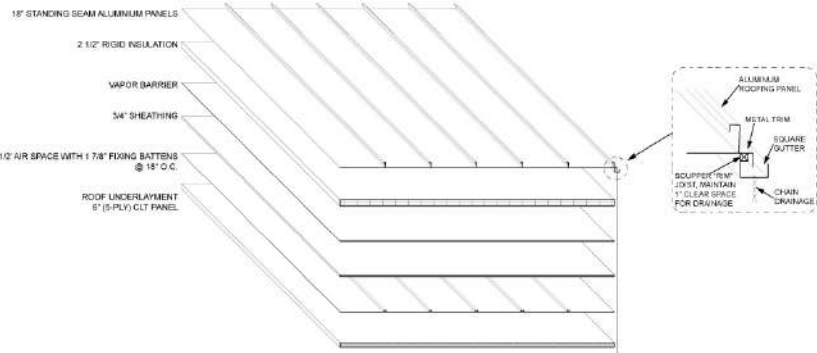


D1 - TYPICAL STRUCTURAL SECTION

1/2" = 1'-0"


PROJECT	CLIENT	SITE	TITLE		SHEET
GRIEF HOUSE CONCEPT DESIGN	LOS ANGELES, CA	APPLE VALLEY, CA 92307	DETAILS		A-501
SCALE		DATE	DRAWN BY		

furniture design


Part of contract work with Seviva. Delivered 3d model, rendering, and shop drawing for custom table fabrication. For commercial client in Los Angeles. Modelled with Rhino 3D, drawn with Revit.

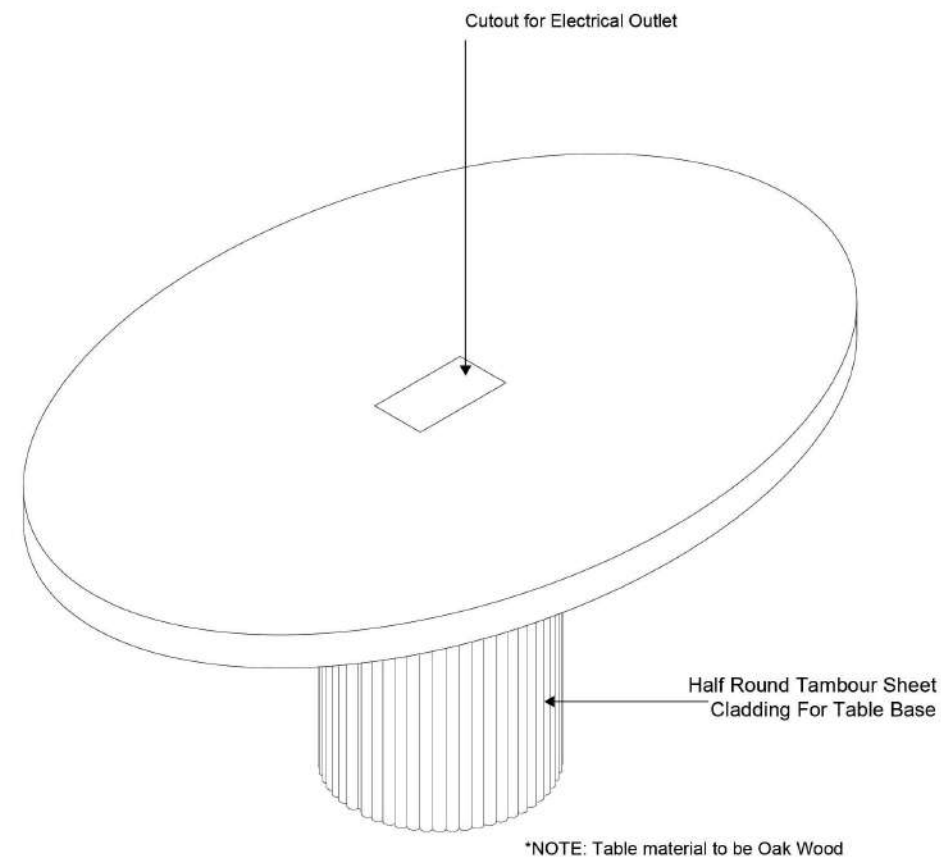


④ Conference Table 3D View
3/4" = 1'-0"

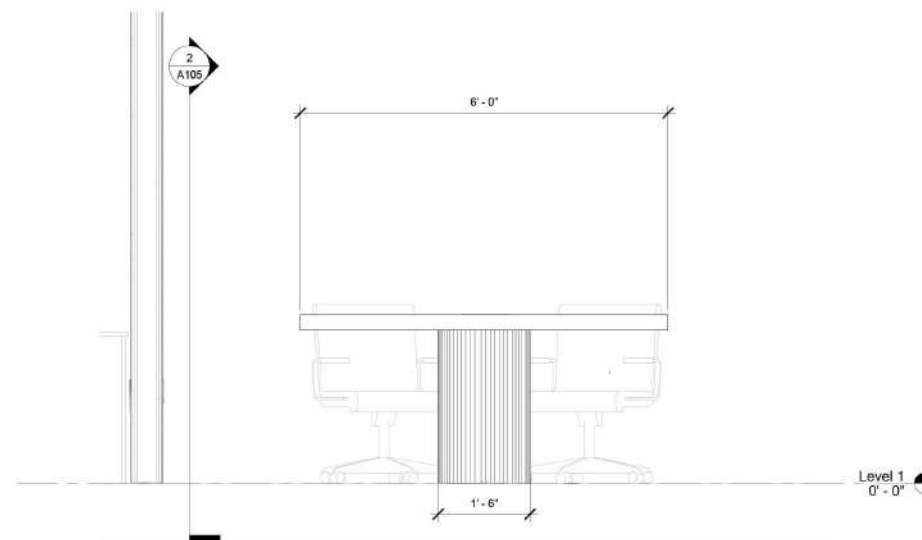


③ Conference Table Front View
3/4" = 1'-0"

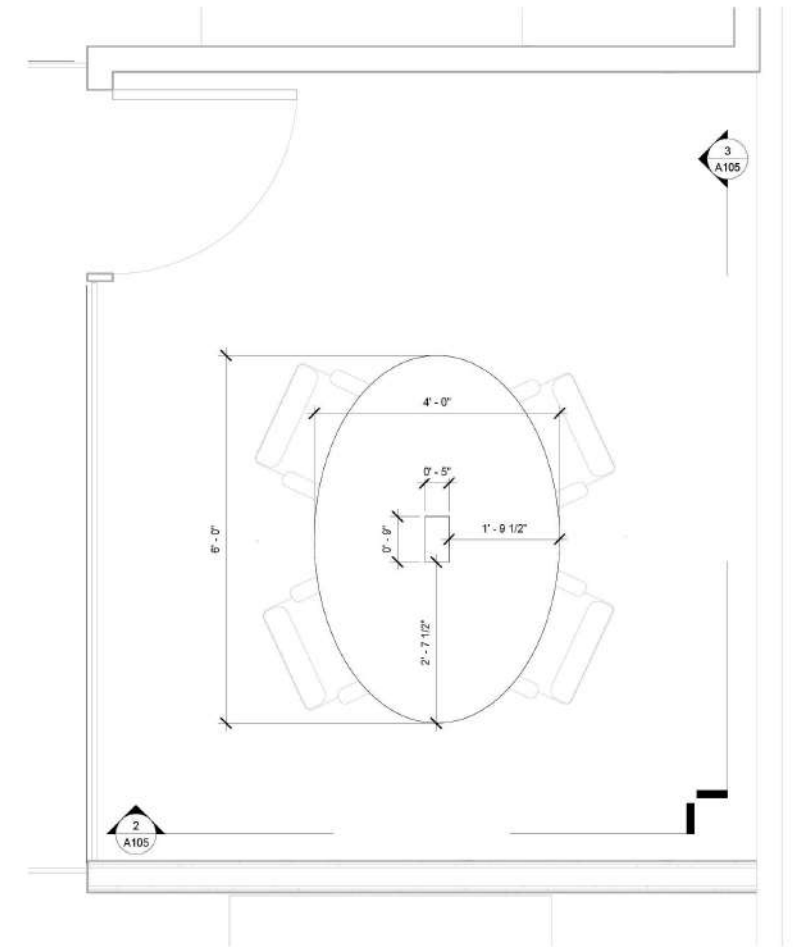

① Conference Table
3/4" = 1'-0"

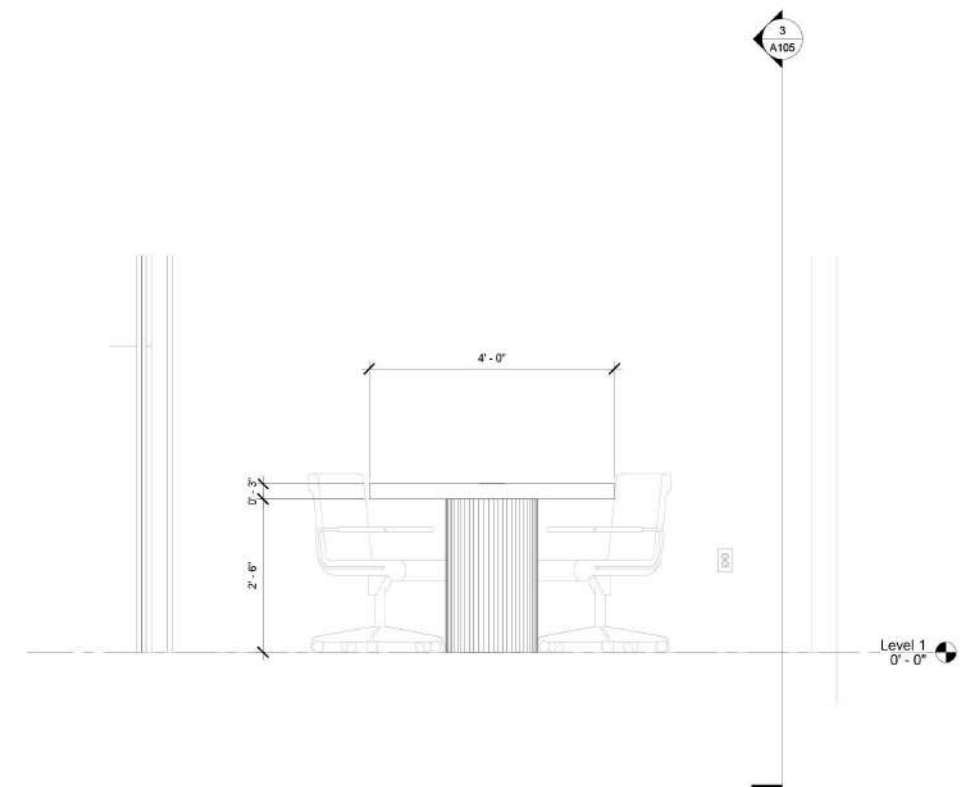


② Conference Table Side View
3/4" = 1'-0"

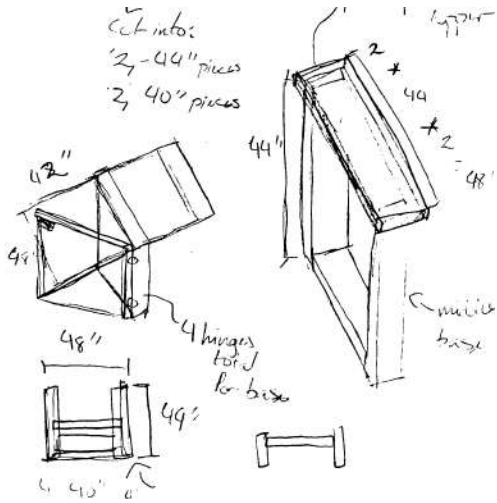


Initial Sketch


Private work. Designed, modelled and fabricated large custom worktable. For use in Los Angeles. Modelled with Rhino 3D, drawn with AutoCAD.

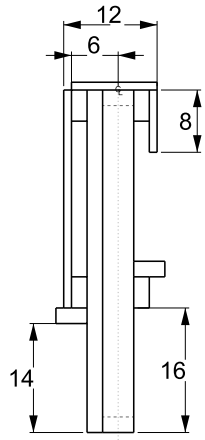

② SIDE VIEW, FOLDED
1/2" = 1'0"

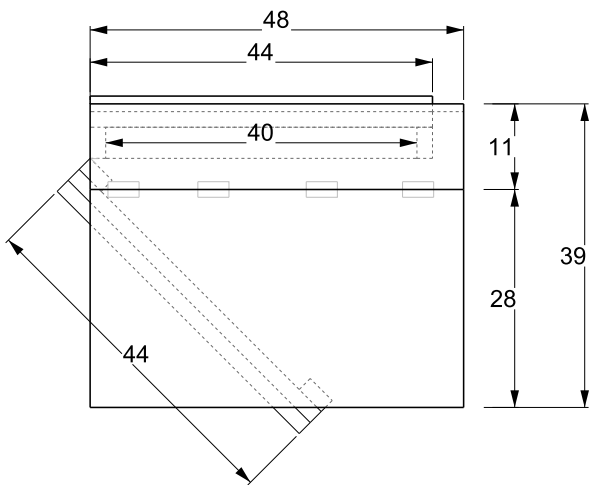

① TOP VIEW, UNFOLDED
1/2" = 1'0"

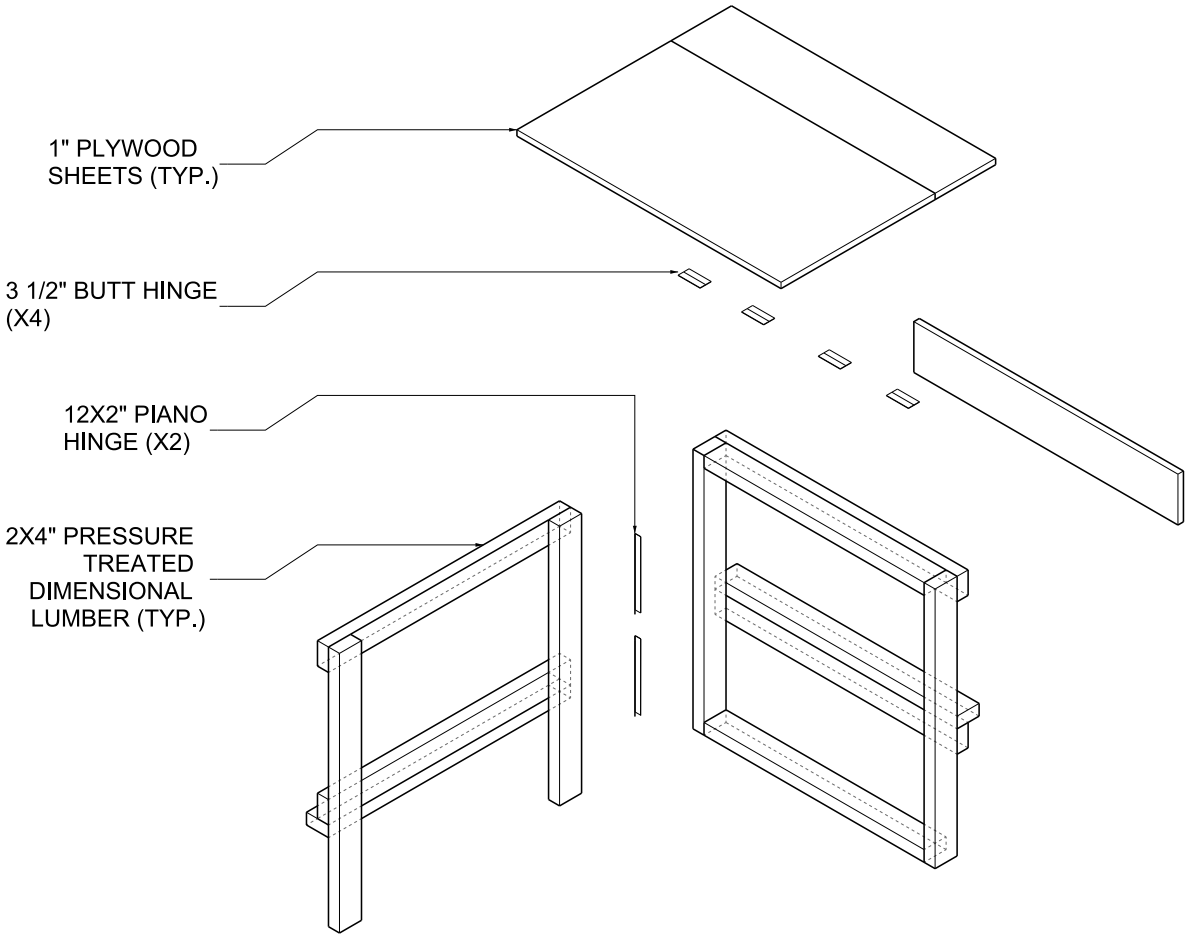

③ ASSEMBLY
1/2" = 1'0"


Fort Homes

Client work; concept design and drawing set detailing modular housing and planned communities in Southern California. Delivered renderings, architectural drawings and diagrams. Done with Rhino 3d, Adobe Illustrator, and Vray.


626 N Wilton Place

Lot: 13,000 sf
15 Units
9 500 sf Classic Cottage Units
4 860 sf Bungalow Entertainment Units
2 500 sf Garden Cottage Units



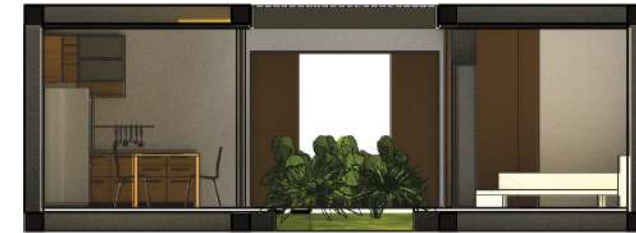

Garden module - 1 bedroom with kitchen and outdoor area, partially enclosed to allow natural light, water, and air to nourish small garden space.

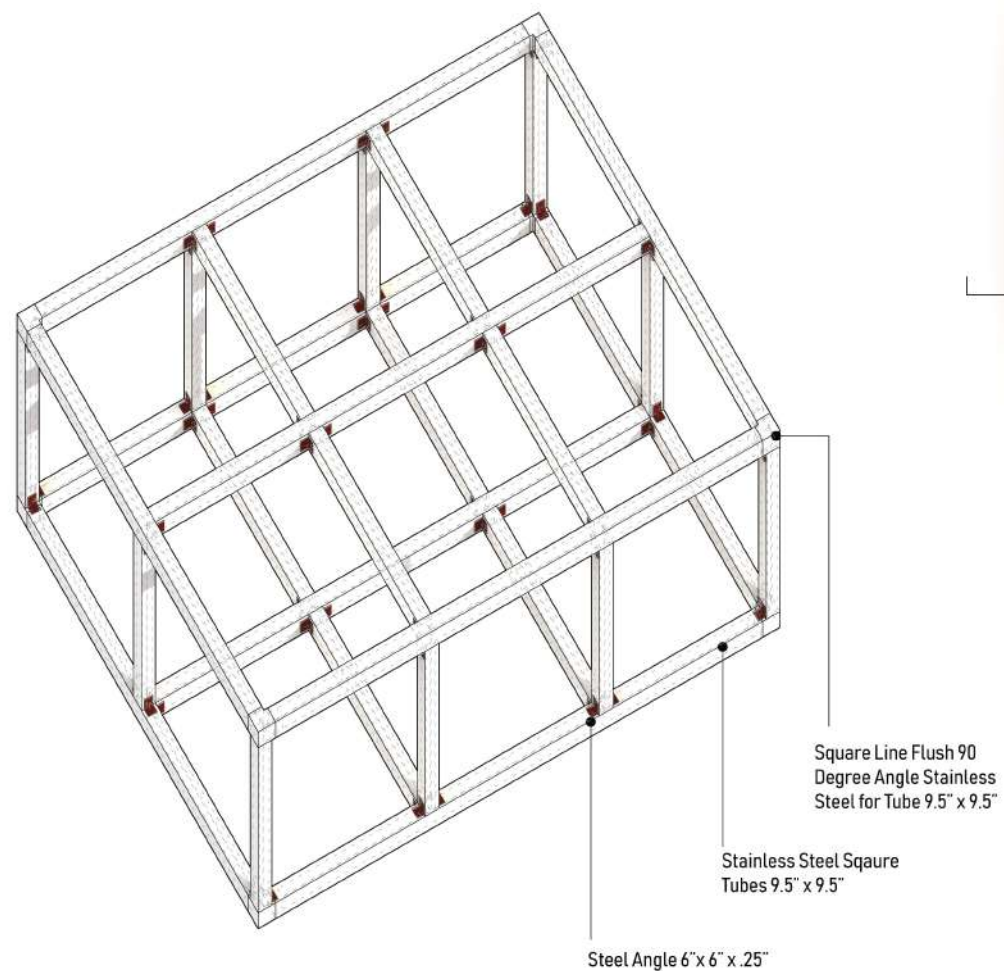

typical steel framing

